

ELEVATION (VIEWED FROM OUTSIDE) 1:20

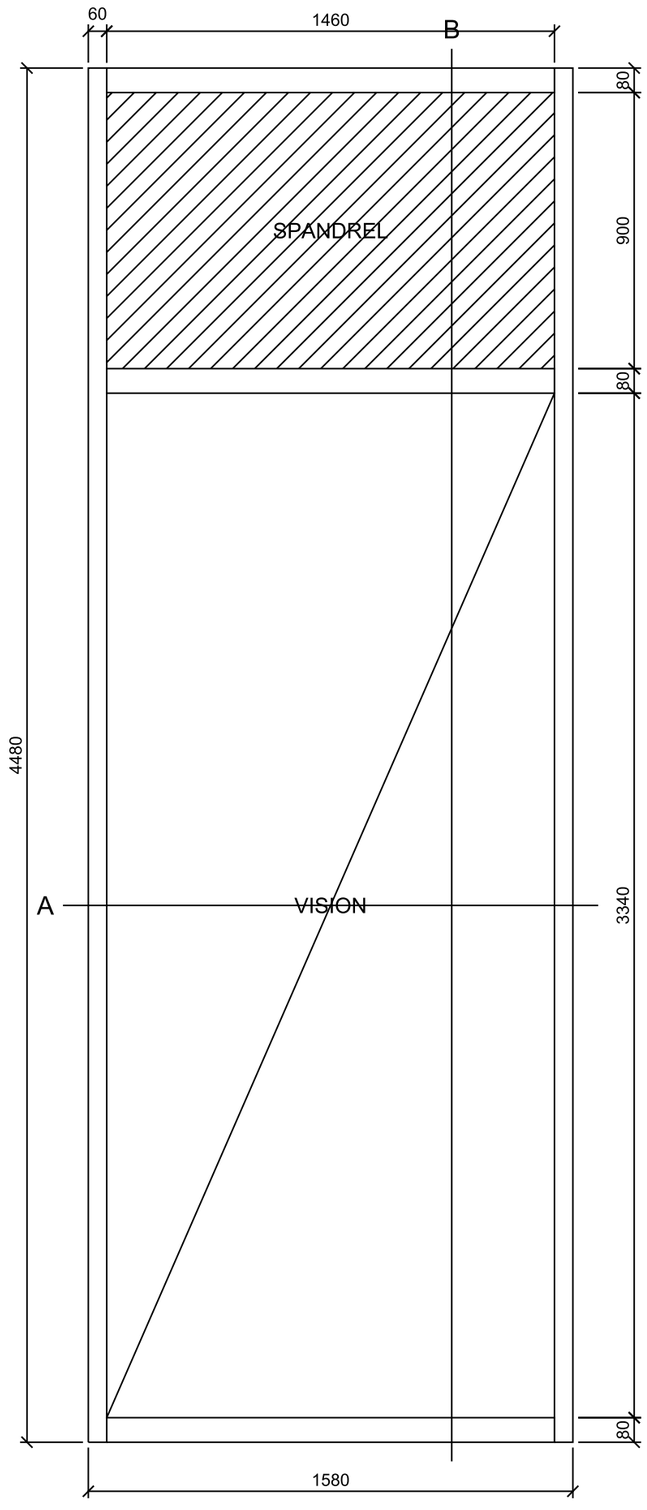


PANEL MARK U1 (88 No.)
1580 x 4480 mm

SECTION A - HORIZONTAL AT VERTICAL JOINT 1:5

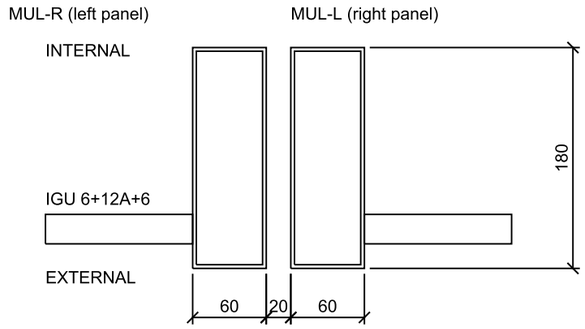

SECTION B - VERTICAL AT STACK JOINT 1:5

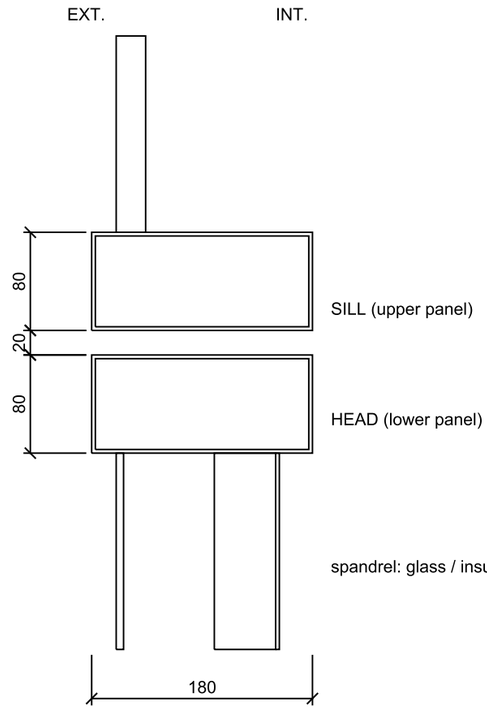

MEMBER SCHEDULE (PER PANEL / TOTAL)


MUL-L L=4480 1/panel 88 total
MUL-R L=4480 1/panel 88 total
SILL L=1460 1/panel 88 total
HEAD L=1460 1/panel 88 total
TRANSOM L=1460 1/panel 88 total

NOTES

1. Independent personal project. Fictional building from facade-bim.
2. Profiles are simplified hollow boxes - indicative only, not a supplier system.
3. NOT FOR CONSTRUCTION. All dimensions in mm.
4. Cut length = member length in model; square cuts; no machining allowance.
5. Glass, gaskets, brackets, coping, sealant and anchors are not detailed.


Drawing no.	FSD-SD-101
Title	Unit U1 - Ground-floor standard unit
Panel type	U1
Quantity	88 No.
Scale	1:20 (elevation), 1:5 (sections) @ A3
Revision	P1
Status	INDICATIVE - NOT FOR CONSTRUCTION
Model source	facade-bim @ fac01b7

ELEVATION (VIEWED FROM OUTSIDE) 1:20

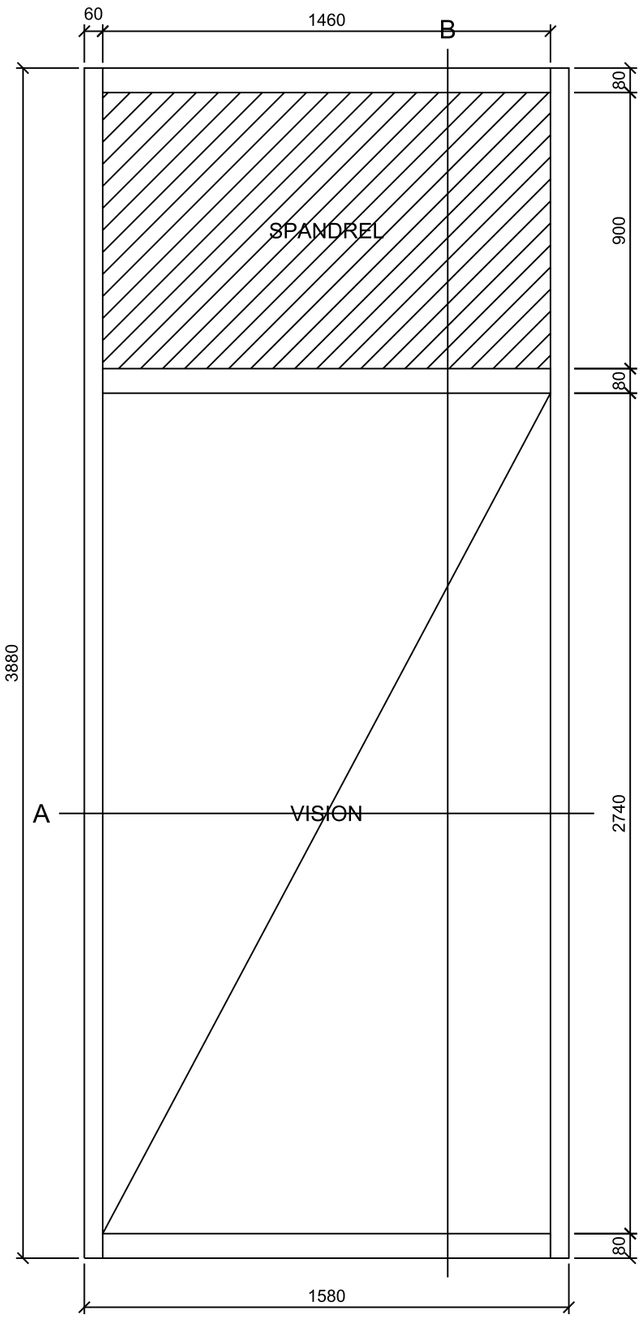


PANEL MARK U2 (620 No.)
1580 x 3880 mm

SECTION A - HORIZONTAL AT VERTICAL JOINT 1:5

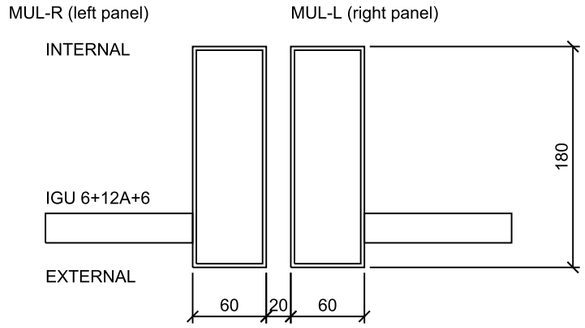

SECTION B - VERTICAL AT STACK JOINT 1:5

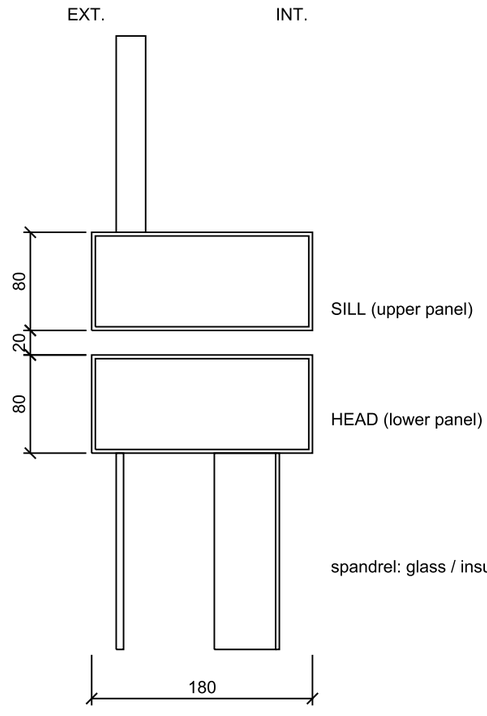

MEMBER SCHEDULE (PER PANEL / TOTAL)


MUL-L L=3880 1/panel 620 total
MUL-R L=3880 1/panel 620 total
SILL L=1460 1/panel 620 total
HEAD L=1460 1/panel 620 total
TRANSOM L=1460 1/panel 620 total

NOTES


1. Independent personal project. Fictional building from facade-bim.
2. Profiles are simplified hollow boxes - indicative only, not a supplier system.
3. NOT FOR CONSTRUCTION. All dimensions in mm.
4. Cut length = member length in model; square cuts; no machining allowance.
5. Glass, gaskets, brackets, coping, sealant and anchors are not detailed.

Drawing no.	FSD-SD-102
Title	Unit U2 - Typical-floor unit
Panel type	U2
Quantity	620 No.
Scale	1:20 (elevation), 1:5 (sections) @ A3
Revision	P1
Status	INDICATIVE - NOT FOR CONSTRUCTION
Model source	facade-bim @ fac01b7


ELEVATION (VIEWED FROM OUTSIDE) 1:20

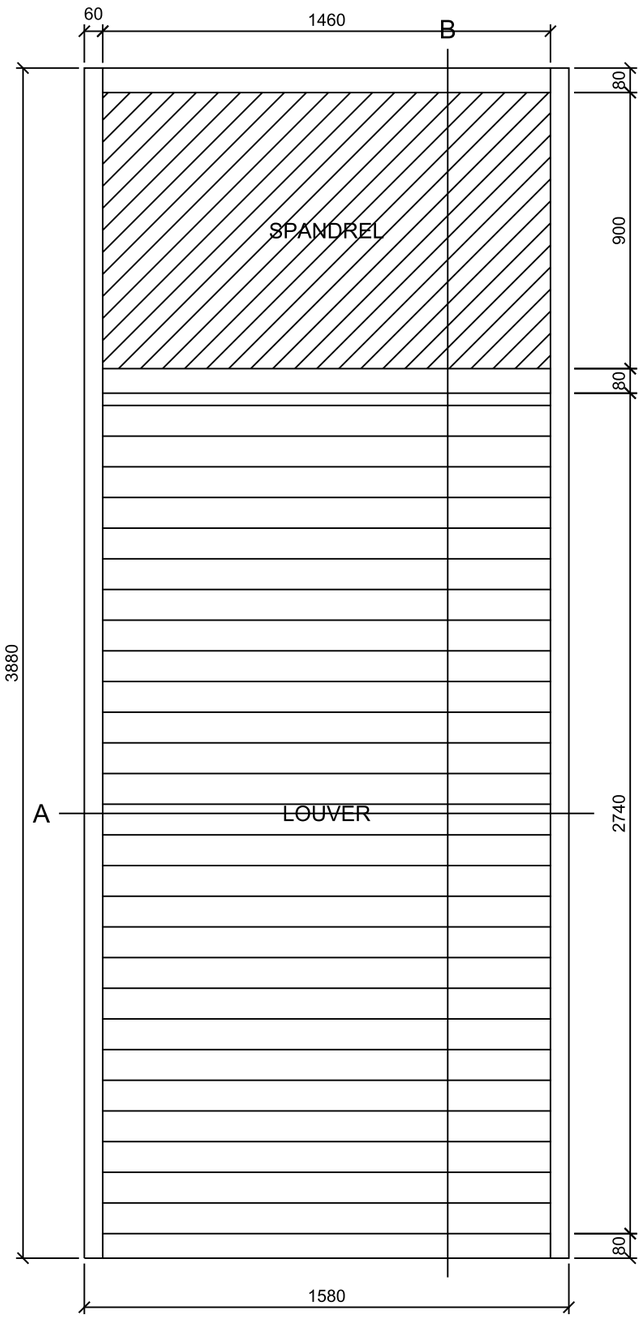

SECTION A - HORIZONTAL AT VERTICAL JOINT 1:5

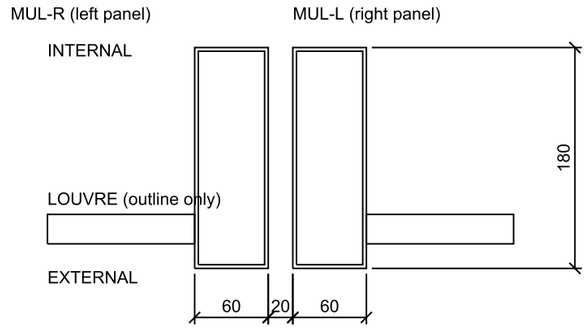

SECTION B - VERTICAL AT STACK JOINT 1:5

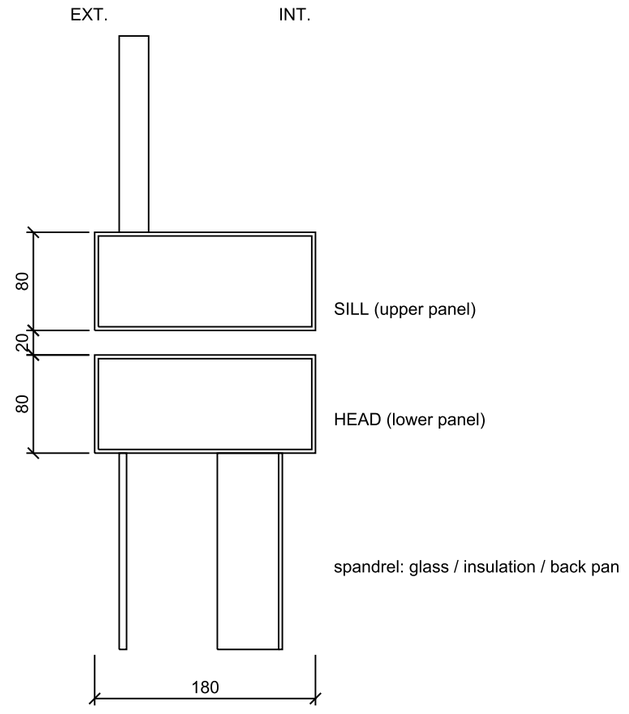

MEMBER SCHEDULE (PER PANEL / TOTAL)

MUL-L L=3880 1/panel 10 total
MUL-R L=3880 1/panel 10 total
SILL L=1460 1/panel 10 total
HEAD L=1460 1/panel 10 total
TRANSOM L=1460 1/panel 10 total

NOTES


1. Independent personal project. Fictional building from facade-bim.
2. Profiles are simplified hollow boxes - indicative only, not a supplier system.
3. NOT FOR CONSTRUCTION. All dimensions in mm.
4. Cut length = member length in model; square cuts; no machining allowance.
5. Glass, gaskets, brackets, coping, sealant and anchors are not detailed.

PANEL MARK U3 (10 No.)

1580 x 3880 mm


Drawing no.	FSD-SD-103
Title	Unit U3 - Plant-room louvre unit
Panel type	U3
Quantity	10 No.
Scale	1:20 (elevation), 1:5 (sections) @ A3
Revision	P1
Status	INDICATIVE - NOT FOR CONSTRUCTION
Model source	facade-bim @ fac01b7

ELEVATION (VIEWED FROM OUTSIDE) 1:20

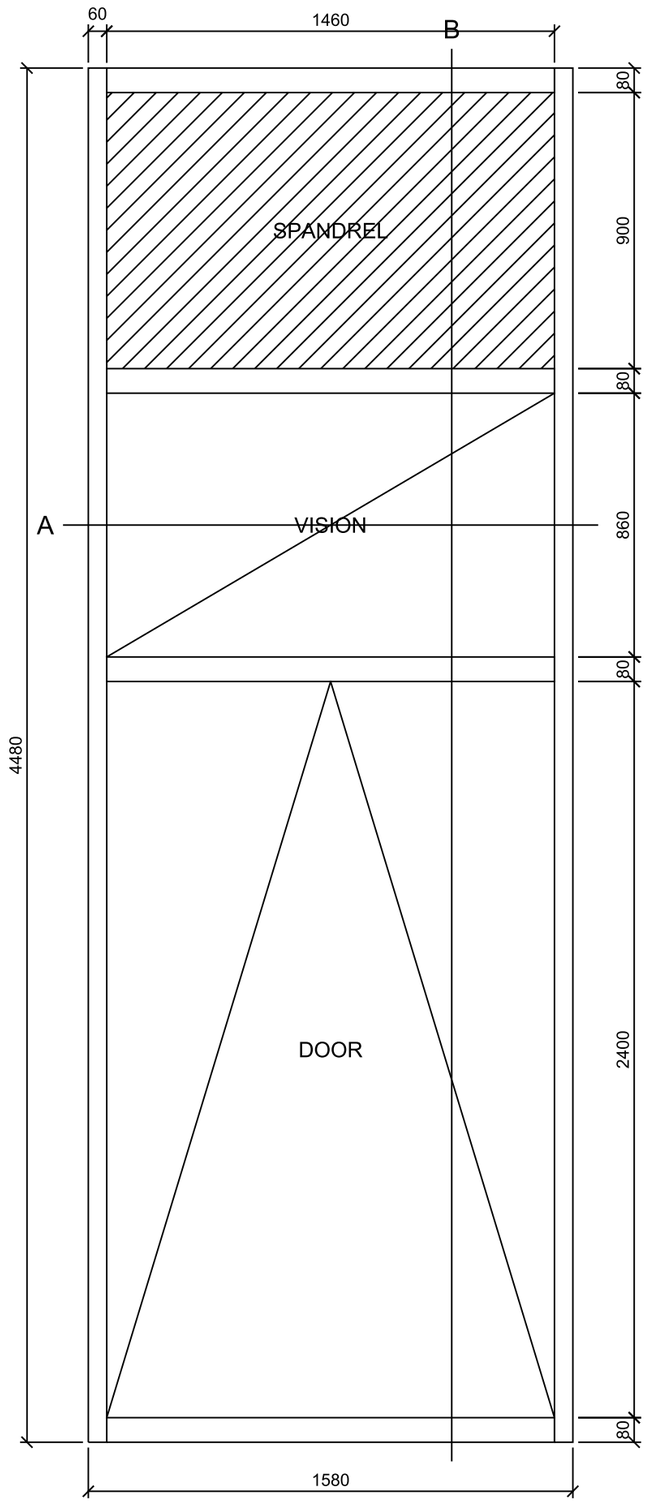


PANEL MARK U4 (2 No.)
1580 x 4480 mm

SECTION A - HORIZONTAL AT VERTICAL JOINT 1:5

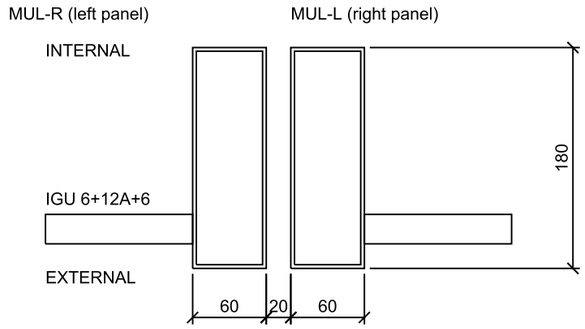

SECTION B - VERTICAL AT STACK JOINT 1:5

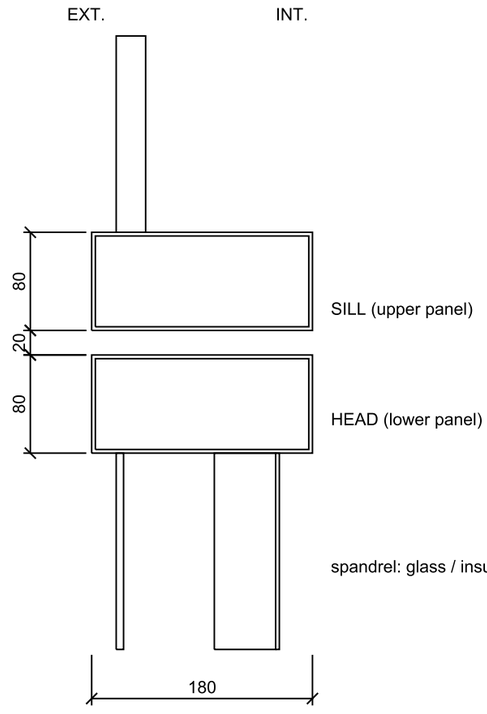

MEMBER SCHEDULE (PER PANEL / TOTAL)


MUL-L L=4480 1/panel 2 total
MUL-R L=4480 1/panel 2 total
SILL L=1460 1/panel 2 total
HEAD L=1460 1/panel 2 total
TRANSOM L=1460 2/panel 4 total

NOTES

1. Independent personal project. Fictional building from facade-bim.
2. Profiles are simplified hollow boxes - indicative only, not a supplier system.
3. NOT FOR CONSTRUCTION. All dimensions in mm.
4. Cut length = member length in model; square cuts; no machining allowance.
5. Glass, gaskets, brackets, coping, sealant and anchors are not detailed.


Drawing no.	FSD-SD-104
Title	Unit U4 - Ground-floor entrance door unit
Panel type	U4
Quantity	2 No.
Scale	1:20 (elevation), 1:5 (sections) @ A3
Revision	P1
Status	INDICATIVE - NOT FOR CONSTRUCTION
Model source	facade-bim @ fac01b7

ELEVATION (VIEWED FROM OUTSIDE) 1:20

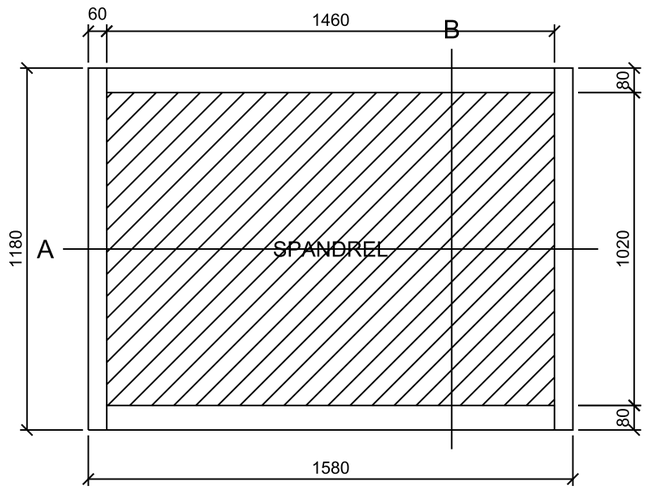


PANEL MARK U5 (90 No.)
1580 x 1180 mm

SECTION A - HORIZONTAL AT VERTICAL JOINT 1:5

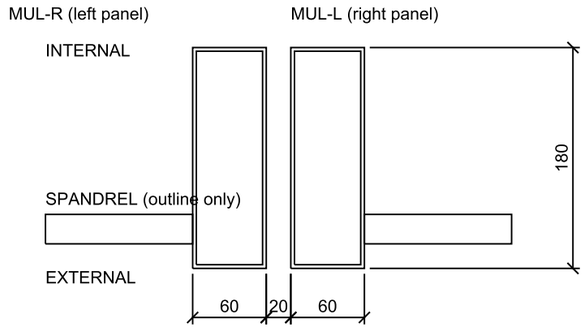

SECTION B - VERTICAL AT STACK JOINT 1:5

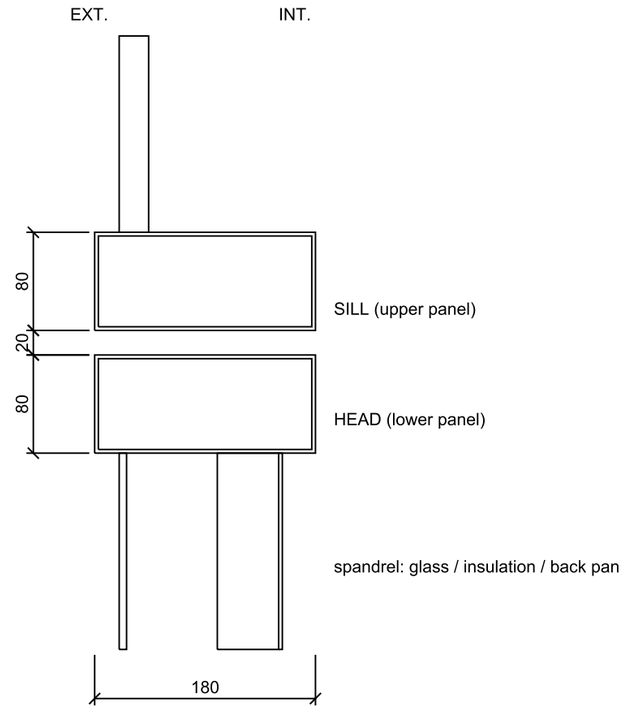

MEMBER SCHEDULE (PER PANEL / TOTAL)

MUL-L L=1180 1/panel 90 total
MUL-R L=1180 1/panel 90 total
SILL L=1460 1/panel 90 total
HEAD L=1460 1/panel 90 total

NOTES

1. Independent personal project. Fictional building from facade-bim.
2. Profiles are simplified hollow boxes - indicative only, not a supplier system.
3. NOT FOR CONSTRUCTION. All dimensions in mm.
4. Cut length = member length in model; square cuts; no machining allowance.
5. Glass, gaskets, brackets, coping, sealant and anchors are not detailed.

Drawing no.	FSD-SD-105
Title	Unit U5 - Parapet unit
Panel type	U5
Quantity	90 No.
Scale	1:20 (elevation), 1:5 (sections) @ A3
Revision	P1
Status	INDICATIVE - NOT FOR CONSTRUCTION
Model source	facade-bim @ fac01b7